


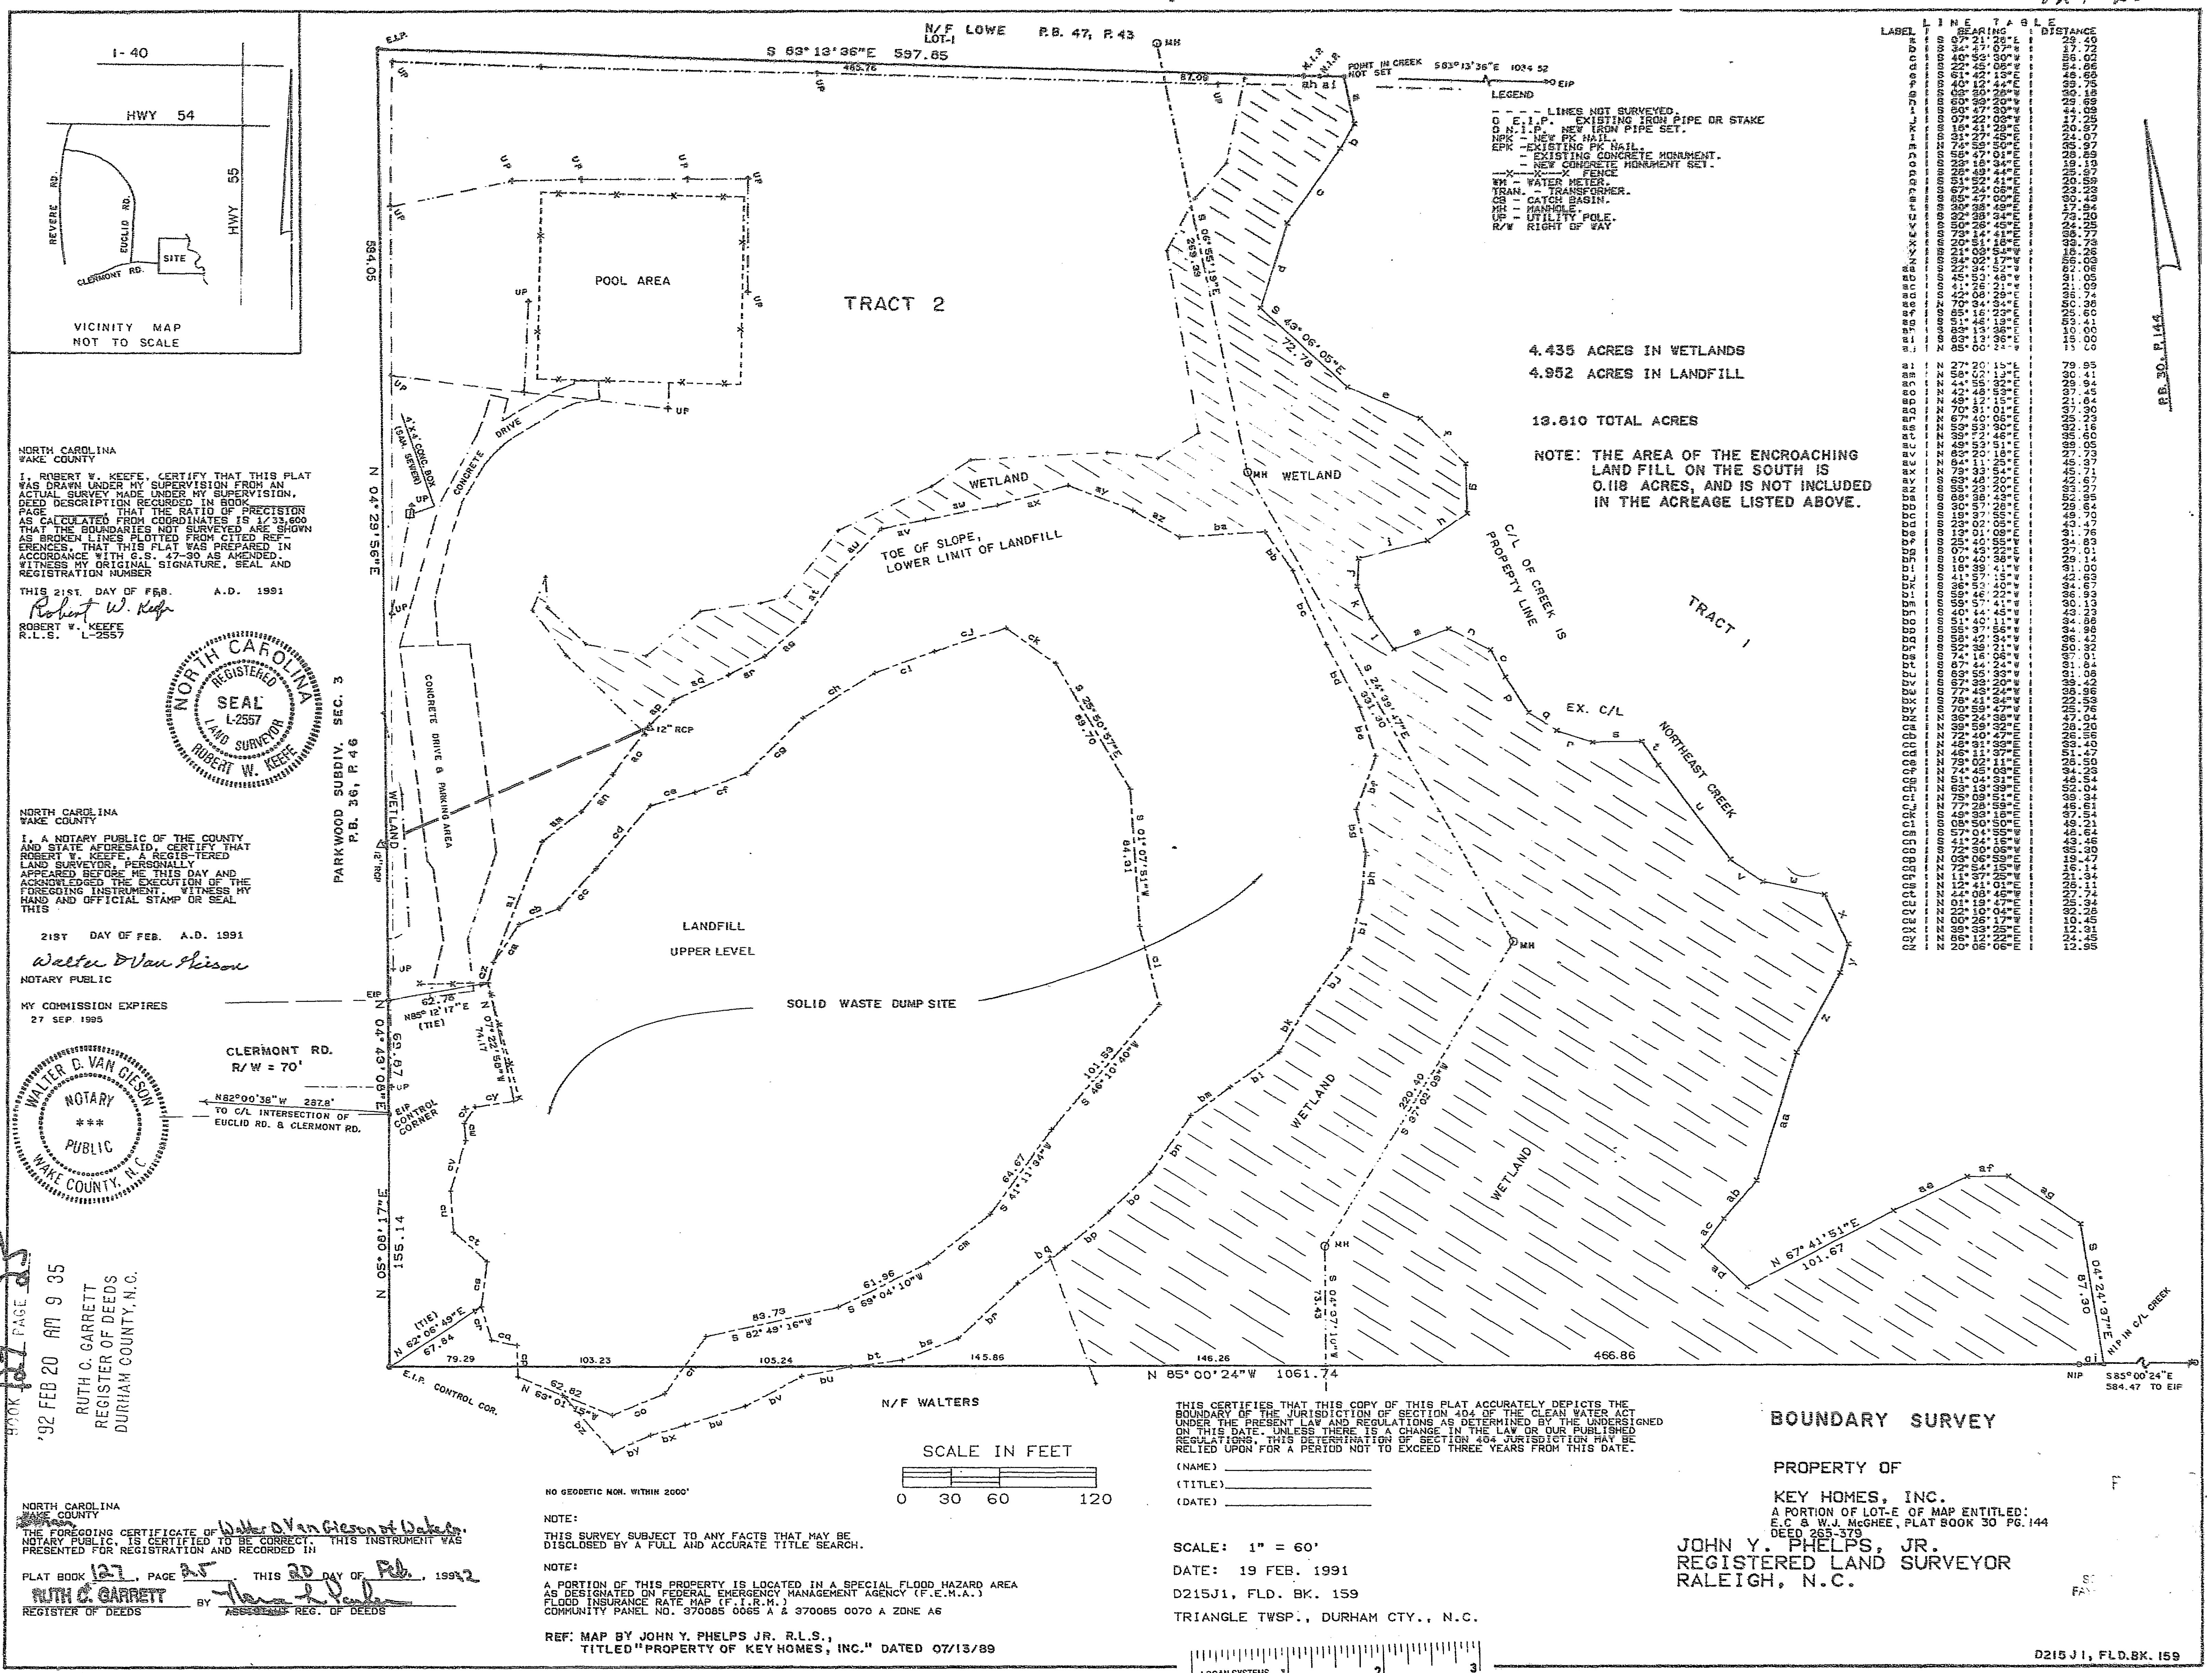


NORTH CAROLINA
WAKE COUNTY

I, ROBERT W. KEEFE, CERTIFY THAT THIS PLAT WAS DRAWN UNDER MY SUPERVISION FROM AN ACTUAL SURVEY MADE UNDER MY SUPERVISION, DEED DESCRIPTION RECORDED IN BOOK PAGE AS CALCULATED THAT THE RATIO OF PRECISION AS CALCULATED FROM COORDINATES IS 1/33,600 THAT THE BOUNDARIES NOT SURVEYED ARE SHOWN AS BROKEN LINES PLOTTED FROM CITED REFERENCES, THAT THIS PLAT WAS PREPARED IN ACCORDANCE WITH G.S. 47-30 AS AMENDED, WITNESS MY ORIGINAL SIGNATURE, SEAL AND REGISTRATION NUMBER

THIS 21ST DAY OF FEB. A.D. 1991

Robert W. Keefe
ROBERT W. KEEFE
R.L.S. L-2557

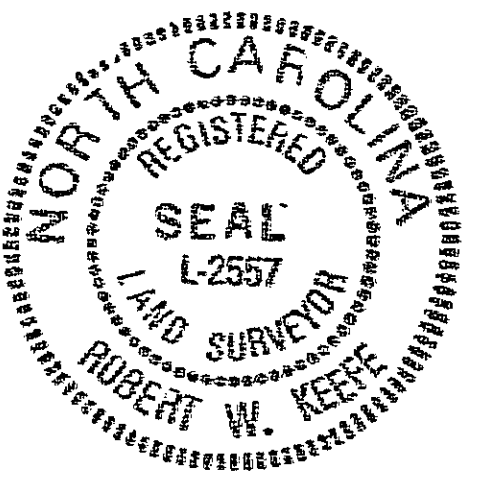


NORTH CAROLINA
WAKE COUNTY

I, A NOTARY PUBLIC OF THE COUNTY AND STATE AFORESAID, CERTIFY THAT ROBERT W. KEEFE, A REGISTERED LAND SURVEYOR, PERSONALLY APPEARED BEFORE ME THIS DAY AND ACKNOWLEDGED THE EXECUTION OF THE FOREGOING INSTRUMENT, WITNESS MY HAND AND OFFICIAL STAMP OR SEAL THIS

21ST DAY OF FEB. A.D. 1991

Walter D. Van Gieson
WALTER D. VAN GIESON
NOTARY PUBLIC

MY COMMISSION EXPIRES
27 SEP. 1995

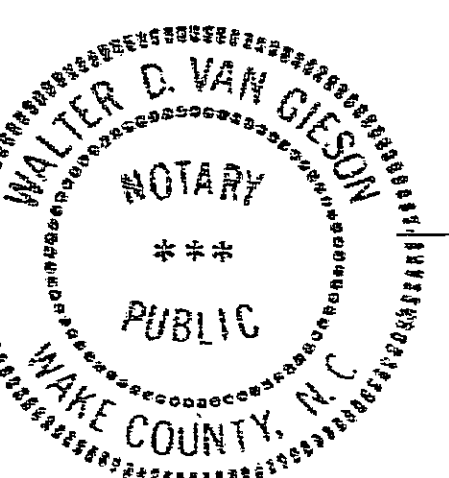

FILED
BOOK 127 PAGE 25
'92 FEB 20 AM 9 35
RUTH C. GARRETT
REGISTER OF DEEDS
DURHAM COUNTY, N.C.

NORTH CAROLINA
WAKE COUNTY

THE FOREGOING CERTIFICATE OF *Walter D. Van Gieson* of Wake County, Notary Public, IS CERTIFIED TO BE CORRECT. THIS INSTRUMENT WAS PRESENTED FOR REGISTRATION AND RECORDED IN

PLAT BOOK 127, PAGE 25, THIS 20 DAY OF FEB., 1992

Ruth C. Garrett
RUTH C. GARRETT
REGISTER OF DEEDS


BY *Thomas L. Pugh*
THOMAS L. PUGH
REG. OF DEEDS

NO GEODETIC MON. WITHIN 2000'

NOTE:
THIS SURVEY SUBJECT TO ANY FACTS THAT MAY BE DISCLOSED BY A FULL AND ACCURATE TITLE SEARCH.

NOTE:
A PORTION OF THIS PROPERTY IS LOCATED IN A SPECIAL FLOOD HAZARD AREA AS DESIGNATED ON FEDERAL EMERGENCY MANAGEMENT AGENCY (F.E.M.A.) FLOOD INSURANCE RATE MAP (F.I.R.M.) COMMUNITY PANEL NO. 370085 0065 A & 370085 0070 A ZONE A6

REF: MAP BY JOHN Y. PHELPS JR. R.L.S.,
TITLED "PROPERTY OF KEY HOMES, INC." DATED 07/13/89

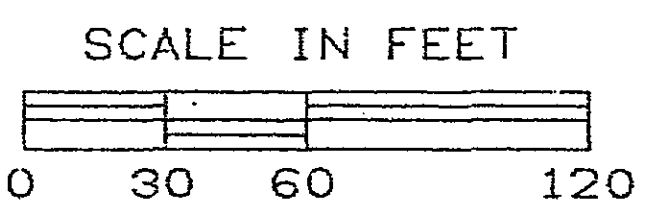

THIS CERTIFIES THAT THIS COPY OF THIS PLAT ACCURATELY DEPICTS THE BOUNDARY OF THE JURISDICTION OF SECTION 404 OF THE CLEAN WATER ACT UNDER THE PRESENT LAW AND REGULATIONS AS DETERMINED BY THE UNDERSIGNED ON THIS DATE. UNLESS THERE IS A CHANGE IN THE LAW OR OUR PUBLISHED REGULATIONS, THIS DETERMINATION OF SECTION 404 JURISDICTION, BE RELIED UPON FOR A PERIOD NOT TO EXCEED THREE YEARS FROM THIS DATE.

(NAME) _____
(TITLE) _____
(DATE) _____

SCALE: 1" = 60'
DATE: 19 FEB. 1991
D215J1, FLD. BK. 159
TRIANGLE TWSP., DURHAM CTY., N.C.

BOUNDARY SURVEY

PROPERTY OF
KEY HOMES, INC.
A PORTION OF LOT-E OF MAP ENTITLED:
F.C.S. W.J. McNEE, PLAT BOOK 30 PG. 144
DEED 265-379

JOHN Y. PHELPS, JR.
REGISTERED LAND SURVEYOR
RALEIGH, N.C.

